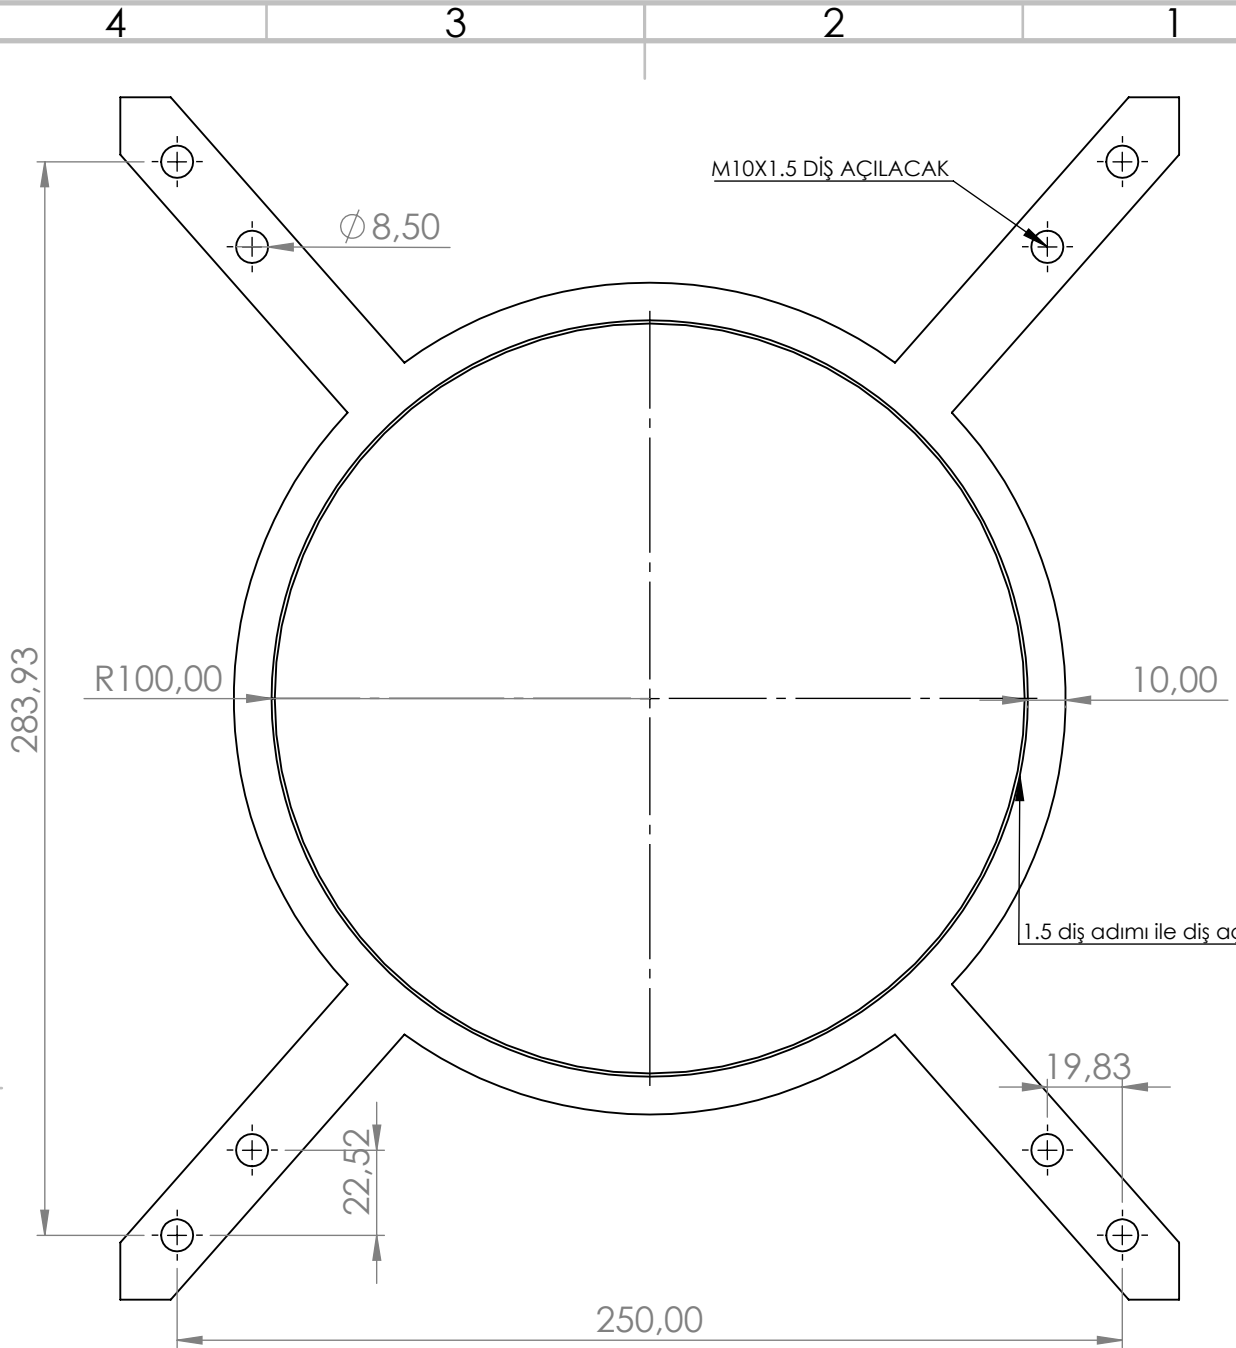


AKSİ BELİRTİLMEDİĞİ SÜRECE: BOYUTLAR MİLMETREDİR YÜZEY CİLASI: TOLERANSLAR: DOĞRUSAL: AÇISAL:		BİTİRME:		KESKİN KENARLARI PAHLAYIN VE KIRIN		TEKNİK RESMİ ÖLÇEKLENDİRMEYİN		REVİZYON	
İSİM		İMZA		TARİH		BAŞLIK:			
ÇİZEN									
DENET.									
ONAY.									
ÜRET.									
KALİTE									
MALZEME:				RESİM NO.				A3	
AĞIRLIK:				ÖLÇEK: 1:10				SAYFA 1 / 1	

3 adet lazer sonrası dış açma